


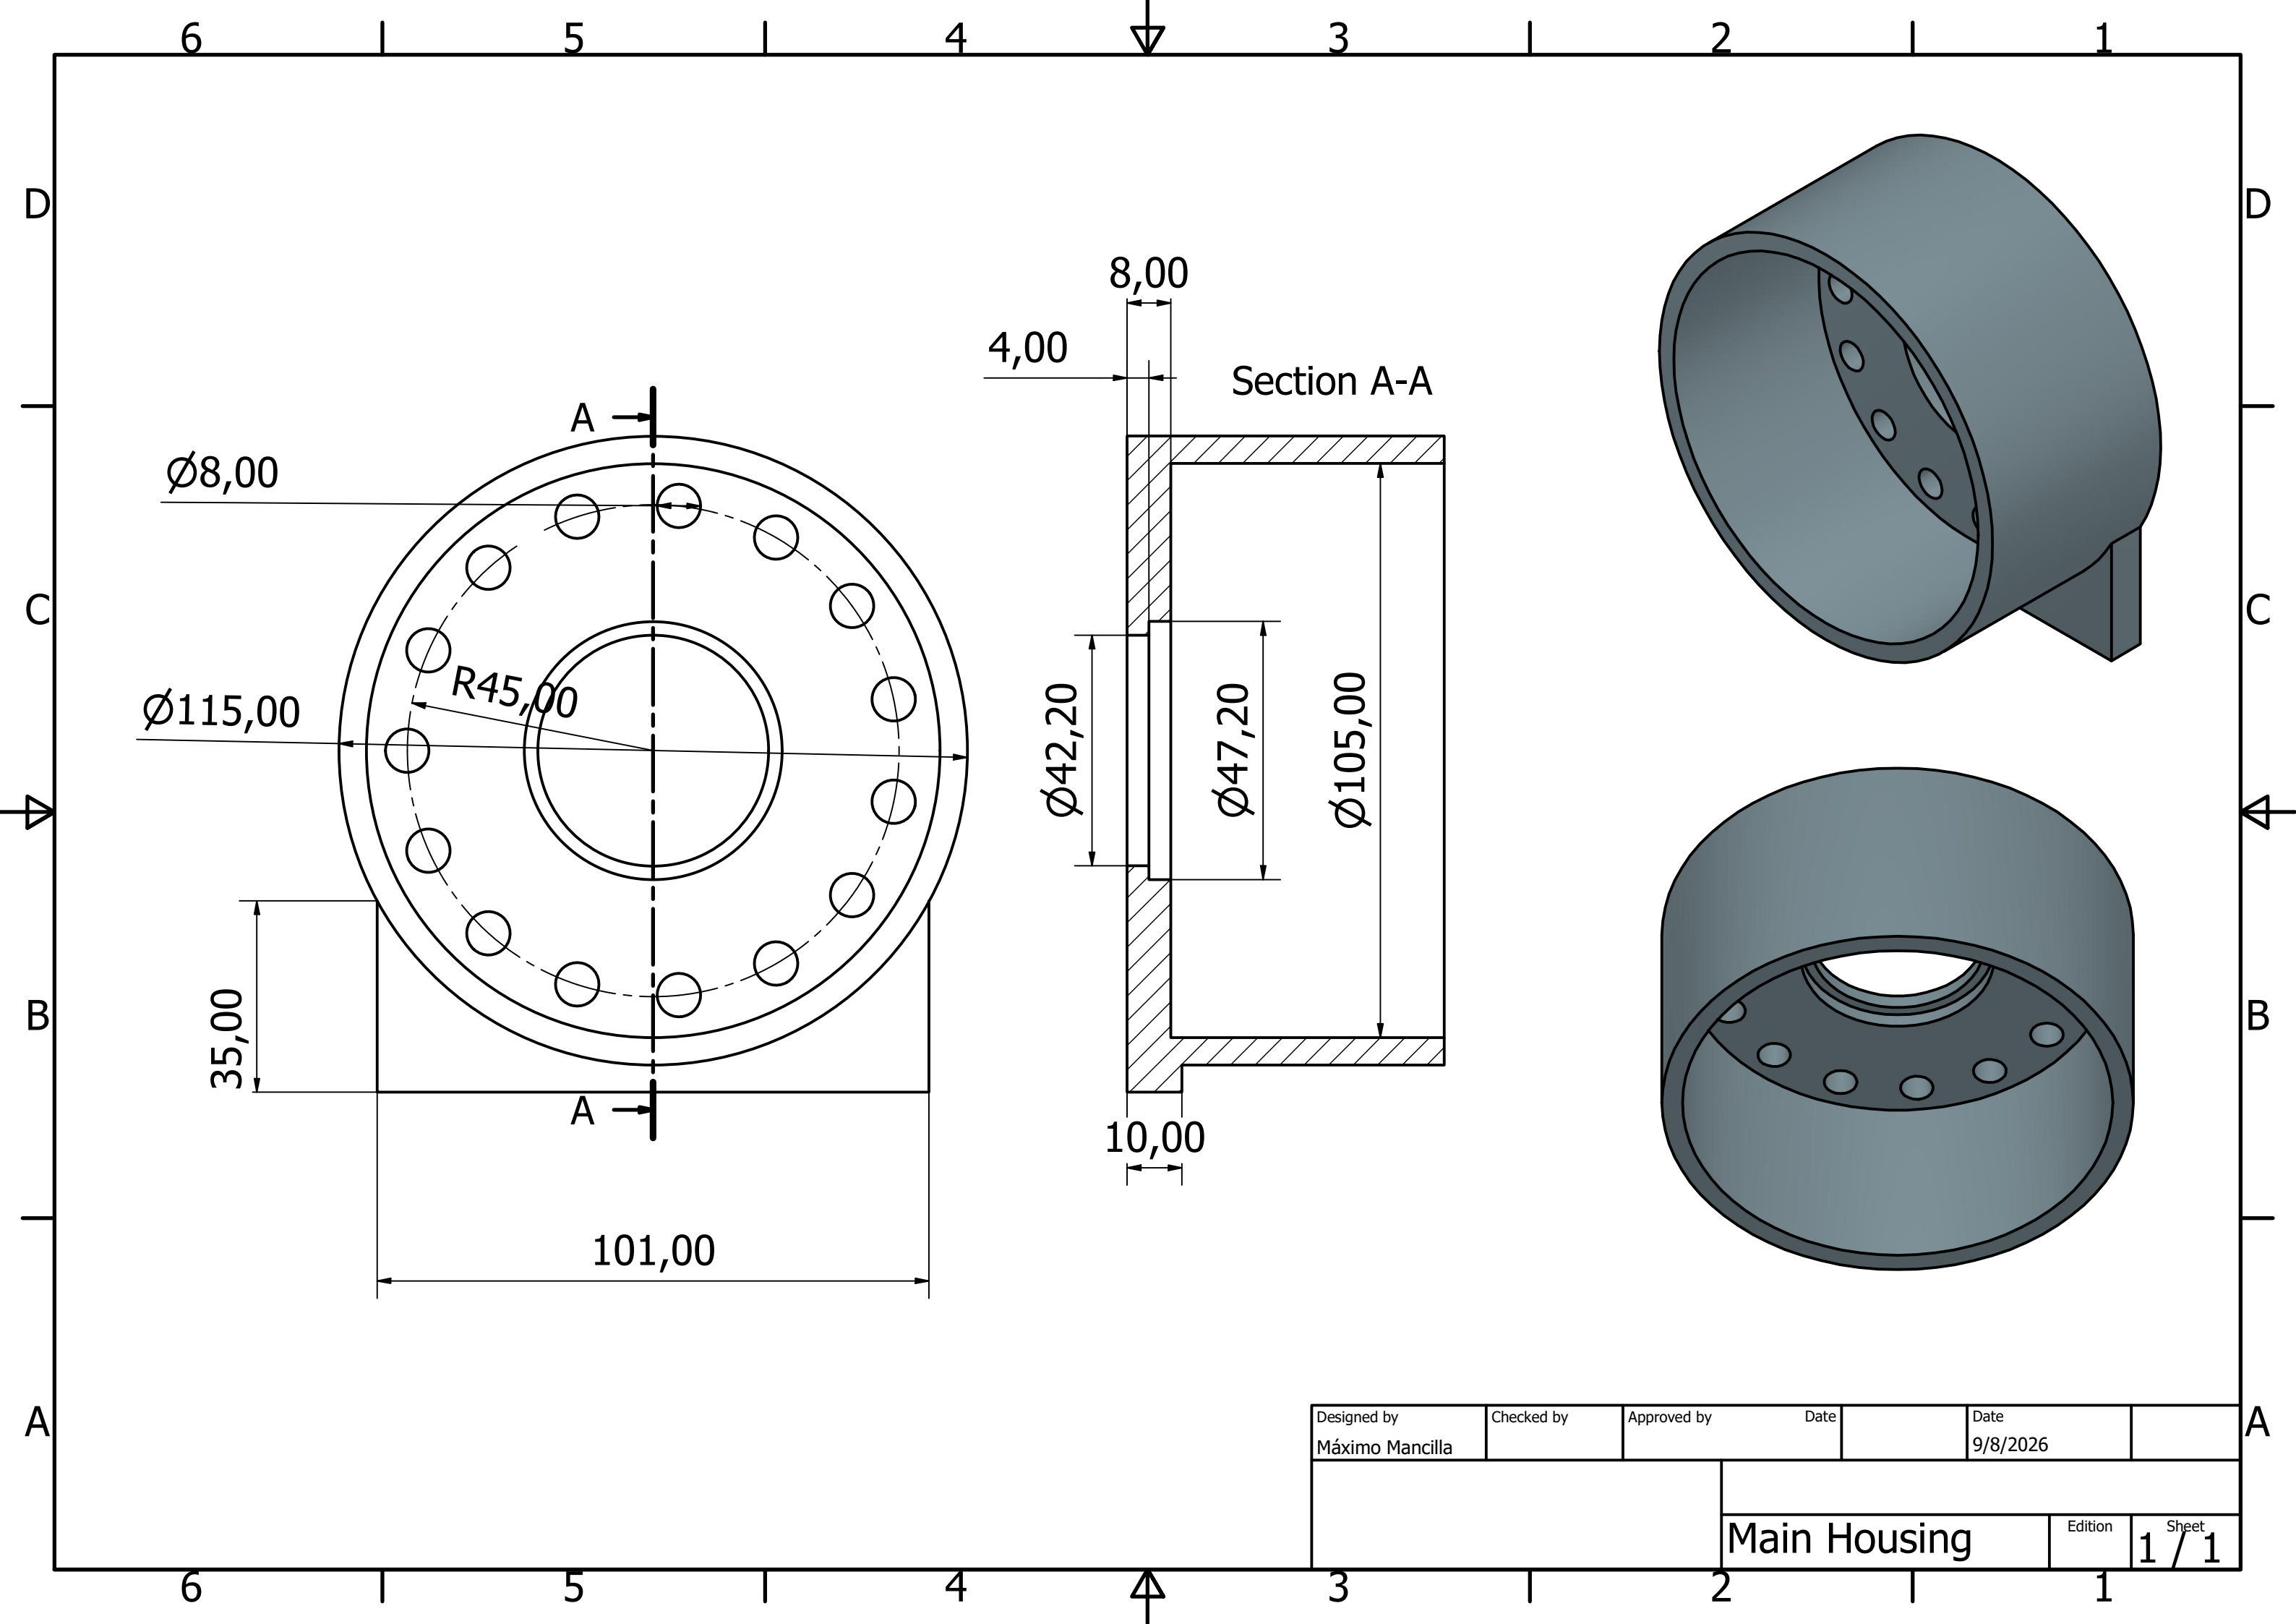

Designed by Máximo Mancilla	Checked by	Approved by	Date		Date 9/8/2026	
			Main Housing		Edition	Sheet 1 / 1